แบบติดตั้งระบบผลิตไฟฟ้าด้วยเซลล์แสงอาทิตย์บนหลังคาขนาด 65.79 kWp.

น้ำดีมไอดอล

PV-SOLAR ROOFTOP

SHOP DWG.


Date: 05 October 2026


SOLAR WING ENERGY CO.,LTD

555 Nikhom Song Khor,Mueang Udon Thani District,

Udon Thani 41000

Tel.080-329-9777

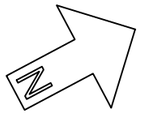

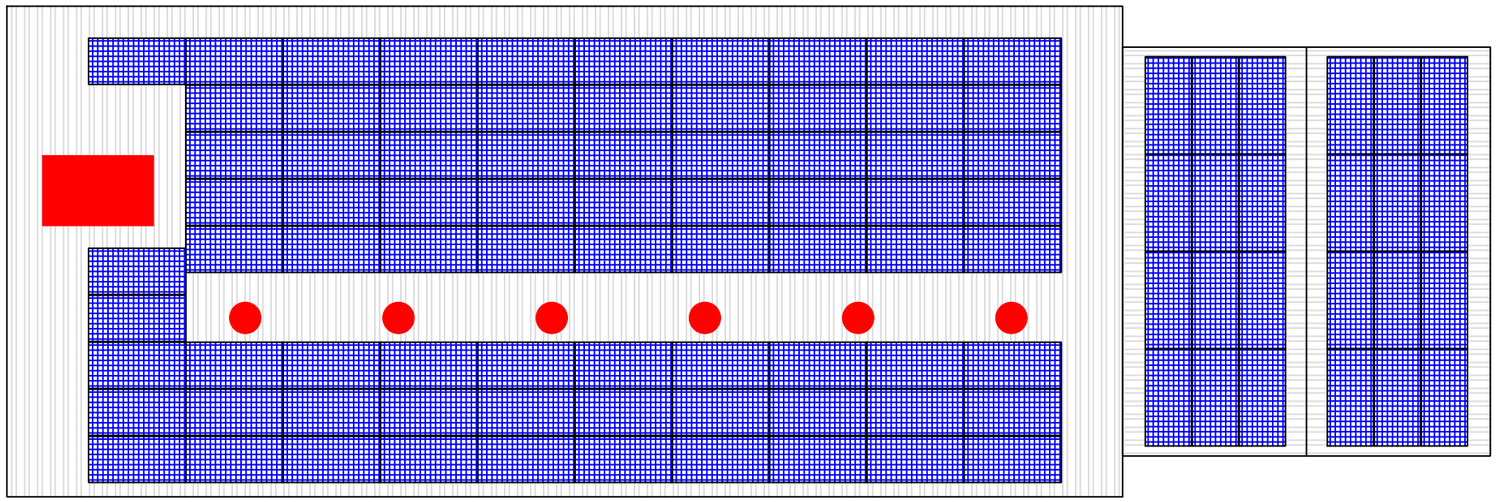


NOTE:

PV MODULE

WALK WAY

Wire Way HDG.


WATER PIPE (PPR)

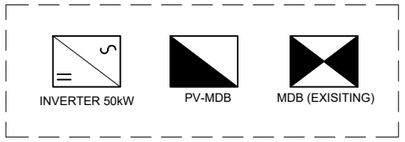

PV MODULE AND STRING INVERTER DESCRIPTION

	NAME : PV Module Type : Mono Halfcell-cut 645Wp Brand : LONGI
	NAME : String Inverter Brand : Huawei Model : SUN2000-50KTL-M3 System Voltage : 380/400V Frequency : 50Hz Protection : DC Disconnecting Switch AC Overcurrent, Anti-Islanding, DC Revers polarity ,DC and AC Surge arrester Residual Current monitoring

SUMMARY FOR INVERTER	
MODULE TYPE	645 Wp
PV MODULE	102 MODULE
NUMBER OF MODULE/STRING	12,14,16 MODULE
TOTAL OF STRING	7 STRING
INSTALL CAPACITY	65.79 kWp
INVERTER RATED	20, 50 kW
NUMBER OF INVERTER	2 UNIT

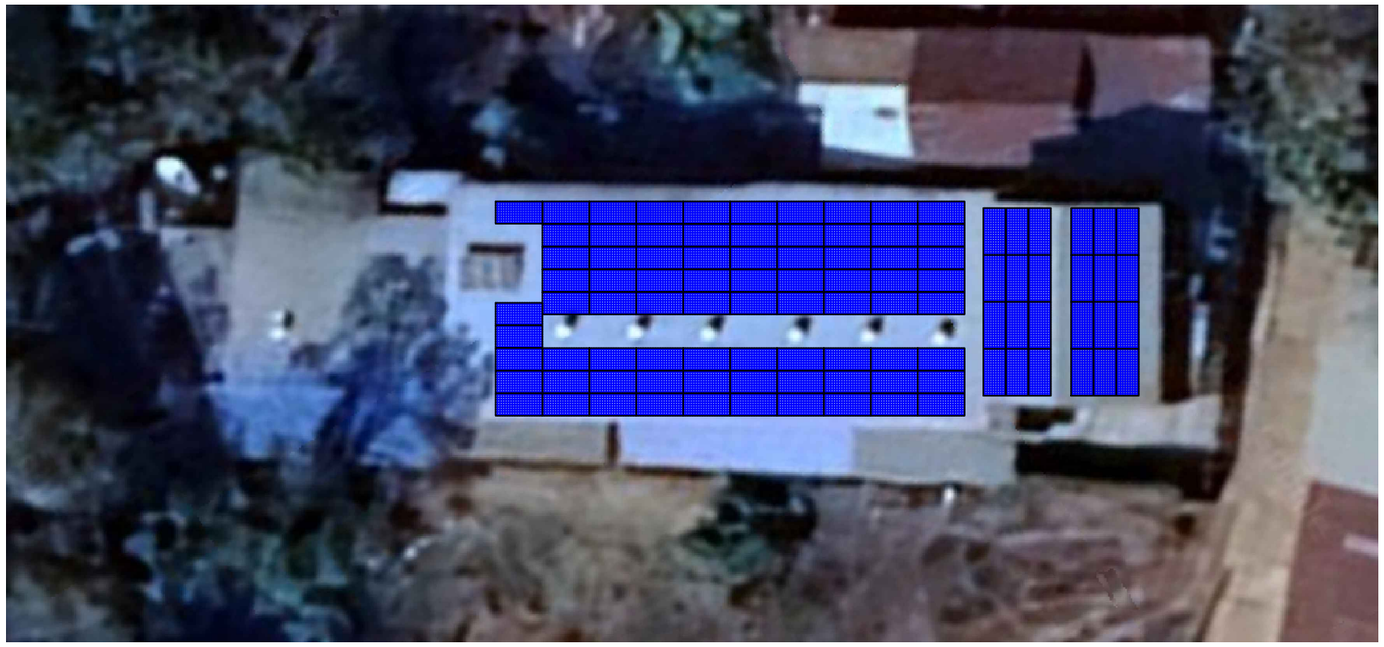

แผนที่โดยสังเขป : 17.838040990035104, 102.57121469864056

SOLAR WING

บริษัท โซลาร์ วิง เอนเนอร์ยี จำกัด
555 หมู่ที่ 1 ต.นิคมสงเคราะห์
อ.เมืองอุดรธานี จ.อุดรธานี 41000

ARCHITECT

CIVIL ENGINEER

ELECTRICAL ENGINEER

ตะวัน กิตติอาสา ภฟก.72980

วนิดา ถำวาปี ภฟก.70838

SANUTARY ENGINEER

PROJECT NO:

SHOP DWG.

PROJECT NAME:

65.79 kWp.
SOLAR PV ROOFTOP


PROJECT OWNER:

น้ำดีมไอดอล

DRAWN:

ตะวัน ภฟก.72980

CHECKED:	
APPROVED:	
SCALE:	1:150
DATE:	05/10/2026
DWG NO:	EE-01
SHEET NO:	

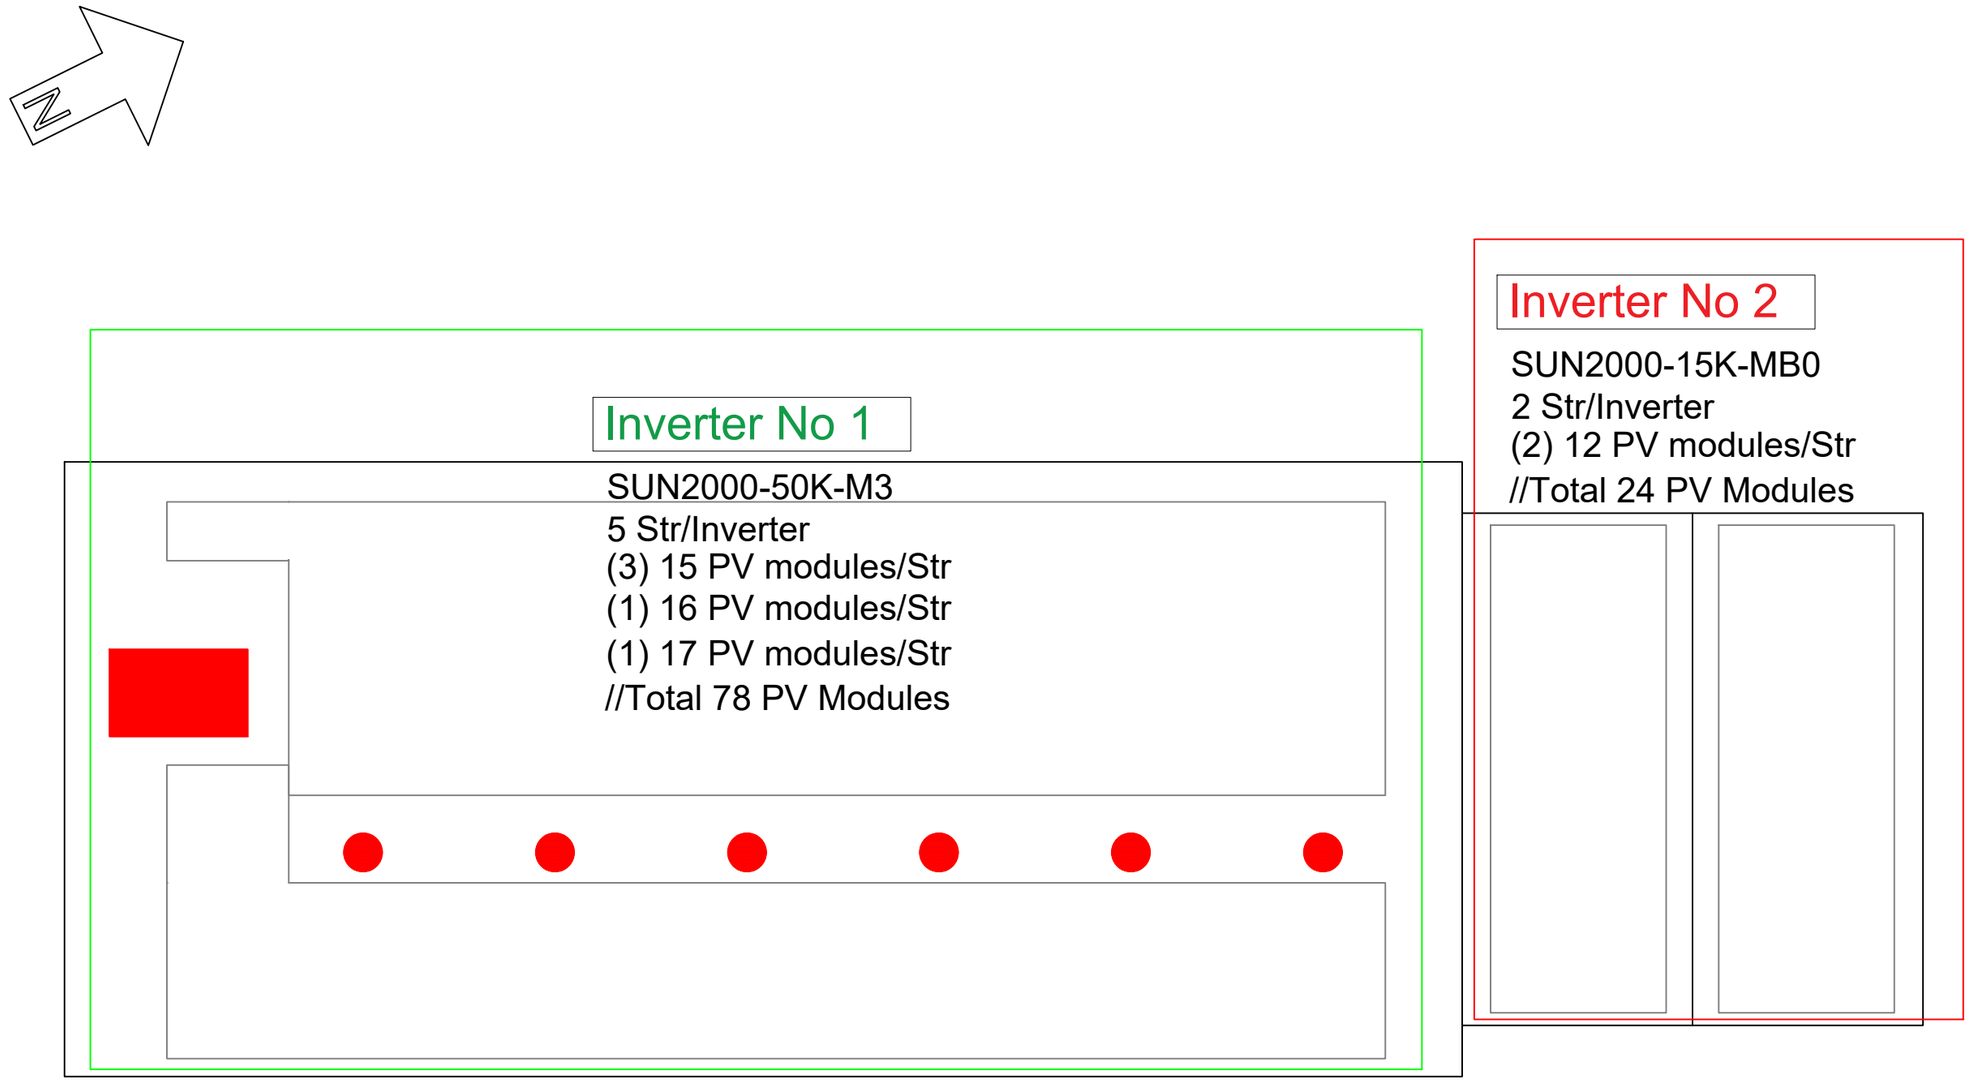


DESIGN PV MODULE

SOLAR WING

บริษัท โซลาร์ วิง เอนเนอร์ยี จำกัด
555 หมู่ที่ 1 ต.นิคมสงเคราะห์
อ.เมืองอุดรธานี จ.อุดรธานี 41000

ARCHITECT	
CIVIL ENGINEER	
ELECTRICAL ENGINEER	ตะวัน กิตติอาสา ภฟก.72980
	วนิดา ถำวาปี ภฟก.70838
SANUTARY ENGINEER	
PROJECT NO:	SHOP DWG.
PROJECT NAME:	65.79 kWp. SOLAR PV ROOFTOP
PROJECT OWNER:	น้ำดีมไอดอล
DRAWN:	ตะวัน ภฟก.72980
CHECKED:	
APPROVED:	
SCALE:	1:120
DATE:	05/10/2026
DWG NO:	EE-02
SHEET NO:	

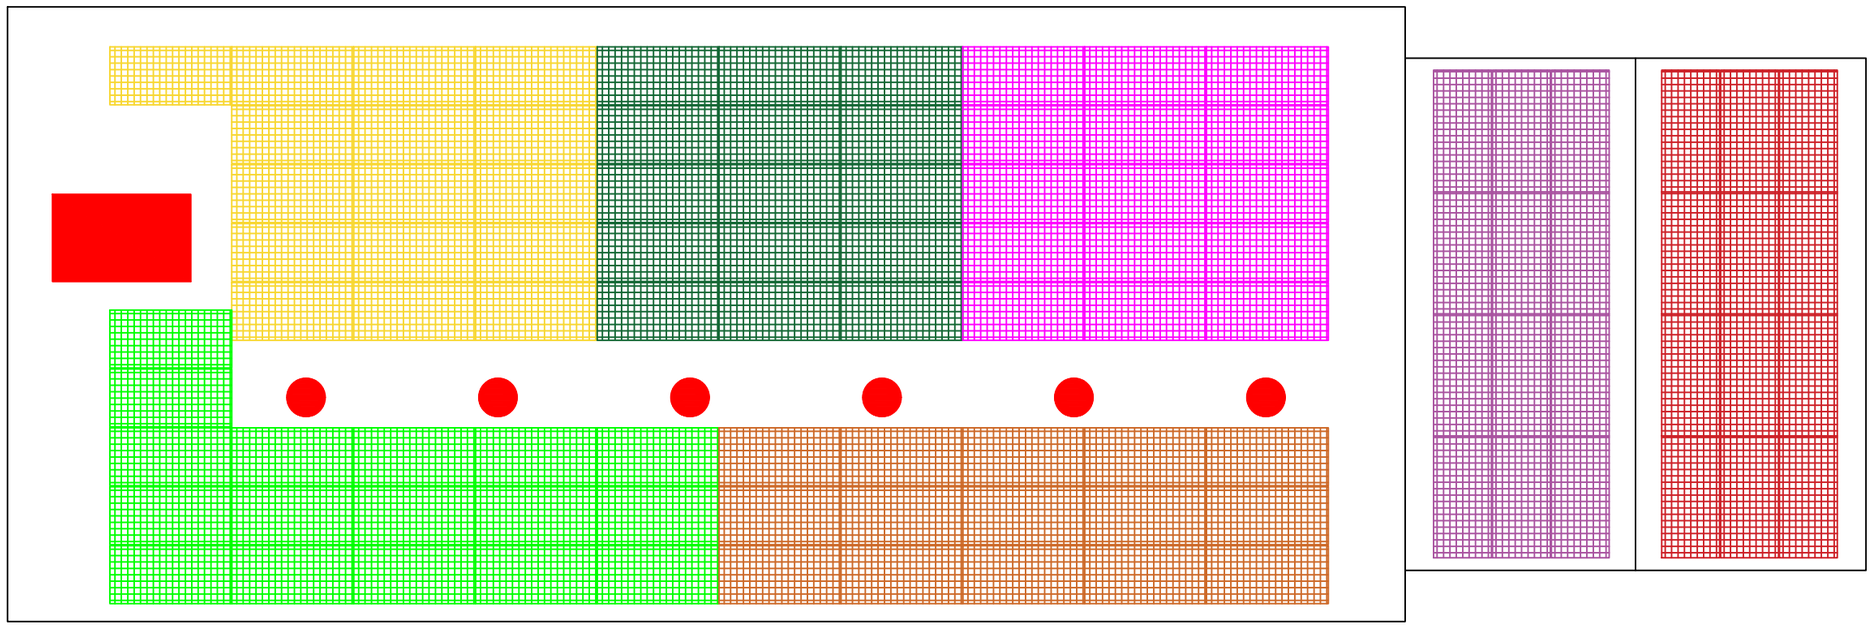


DESIGN PV MODULE

SOLAR WING

บริษัท โซลาร์ วิง เอนเนอร์ยี จำกัด
555 หมู่ที่ 1 ต.นิคมสงเคราะห์
อ.เมืองอุดรธานี จ.อุดรธานี 41000

ARCHITECT	
CIVIL ENGINEER	
ELECTRICAL ENGINEER	ตะวัน กิตติอาสา ภฟก.72980
	วนิดา ถำวาปี ภฟก.70838
SANUTARY ENGINEER	
PROJECT NO:	SHOP DWG.
PROJECT NAME:	65.79 kWp. SOLAR PV ROOFTOP
PROJECT OWNER:	น้ำดีมไอดอล
DRAWN:	ตะวัน ภฟก.72980
CHECKED:	
APPROVED:	
SCALE:	1:120
DATE:	05/10/2026
DWG NO:	EE-02
SHEET NO:	

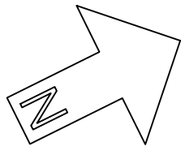

INV - 50KTL STR1 PV 1	INV - 50KTL STR1 PV 2	INV - 50KTL STR1 PV 11	INV - 50KTL STR1 PV 12	INV - 50KTL STR2 PV 1	INV - 50KTL STR2 PV 10	INV - 50KTL STR2 PV 11	INV - 50KTL STR3 PV 1	INV - 50KTL STR3 PV 10	INV - 50KTL STR3 PV 11
	INV - 50KTL STR1 PV 3	INV - 50KTL STR1 PV 10	INV - 50KTL STR1 PV 13	INV - 50KTL STR2 PV 2	INV - 50KTL STR2 PV 9	INV - 50KTL STR2 PV 12	INV - 50KTL STR3 PV 2	INV - 50KTL STR3 PV 9	INV - 50KTL STR3 PV 12
	INV - 50KTL STR1 PV 4	INV - 50KTL STR1 PV 9	INV - 50KTL STR1 PV 14	INV - 50KTL STR2 PV 3	INV - 50KTL STR2 PV 8	INV - 50KTL STR2 PV 13	INV - 50KTL STR3 PV 3	INV - 50KTL STR3 PV 8	INV - 50KTL STR3 PV 13
	INV - 50KTL STR1 PV 5	INV - 50KTL STR1 PV 8	INV - 50KTL STR1 PV 15	INV - 50KTL STR2 PV 4	INV - 50KTL STR2 PV 7	INV - 50KTL STR2 PV 14	INV - 50KTL STR3 PV 4	INV - 50KTL STR3 PV 7	INV - 50KTL STR3 PV 14
	INV - 50KTL STR1 PV 6	INV - 50KTL STR1 PV 7	INV - 50KTL STR1 PV 16	INV - 50KTL STR2 PV 5	INV - 50KTL STR2 PV 6	INV - 50KTL STR2 PV 15	INV - 50KTL STR3 PV 5	INV - 50KTL STR3 PV 6	INV - 50KTL STR3 PV 15
INV - 50KTL STR4 PV 1									
INV - 50KTL STR4 PV 2									
INV - 50KTL STR4 PV 3	INV - 50KTL STR4 PV 8	INV - 50KTL STR4 PV 9	INV - 50KTL STR4 PV 14	INV - 50KTL STR4 PV 15	INV - 50KTL STR5 PV 1	INV - 50KTL STR5 PV 6	INV - 50KTL STR5 PV 7	INV - 50KTL STR5 PV 12	INV - 50KTL STR5 PV 13
INV - 50KTL STR4 PV 4	INV - 50KTL STR4 PV 7	INV - 50KTL STR4 PV 10	INV - 50KTL STR4 PV 13	INV - 50KTL STR4 PV 16	INV - 50KTL STR5 PV 2	INV - 50KTL STR5 PV 5	INV - 50KTL STR5 PV 8	INV - 50KTL STR5 PV 11	INV - 50KTL STR5 PV 14
INV - 50KTL STR4 PV 5	INV - 50KTL STR4 PV 6	INV - 50KTL STR4 PV 11	INV - 50KTL STR4 PV 12	INV - 50KTL STR4 PV 17	INV - 50KTL STR5 PV 3	INV - 50KTL STR5 PV 4	INV - 50KTL STR5 PV 9	INV - 50KTL STR5 PV 10	INV - 50KTL STR5 PV 15

INV - 15KTL STR1 PV 1	INV - 15KTL STR1 PV 2	INV - 15KTL STR1 PV 3	INV - 15KTL STR1 PV 4	INV - 15KTL STR1 PV 5	INV - 15KTL STR1 PV 6	INV - 15KTL STR1 PV 7	INV - 15KTL STR1 PV 8	INV - 15KTL STR1 PV 9	INV - 15KTL STR1 PV 10	INV - 15KTL STR1 PV 11	INV - 15KTL STR1 PV 12

INV - 15KTL STR2 PV 1	INV - 15KTL STR2 PV 2	INV - 15KTL STR2 PV 3	INV - 15KTL STR2 PV 4	INV - 15KTL STR2 PV 5	INV - 15KTL STR2 PV 6	INV - 15KTL STR2 PV 7	INV - 15KTL STR2 PV 8	INV - 15KTL STR2 PV 9	INV - 15KTL STR2 PV 10	INV - 15KTL STR2 PV 11	INV - 15KTL STR2 PV 12

NUMBER OF MODULE/STRING

SOLAR WING

บริษัท โซลาร์ วิง เอนเนอร์ยี จำกัด
555 หมู่ที่ 1 ต.นิคมสงเคราะห์
อ.เมืองอุดรธานี จ.อุดรธานี 41000

ARCHITECT

CIVIL ENGINEER

ELECTRICAL ENGINEER

ตะวัน กิตติอาสา ภฟก.72980

วนิดา ถ้ำวาปี ภฟก.70838

SANUTARY ENGINEER


PROJECT NO:
SHOP DWG.

PROJECT NAME:
65.79 kWp.
SOLAR PV ROOFTOP

PROJECT OWNER:
น้ำดีมไอดอล

DRAWN:
ตะวัน ภฟก.72980

CHECKED:	
APPROVED:	
SCALE:	1:120
DATE:	05/10/2026
DWG NO:	EE-03
SHEET NO:	

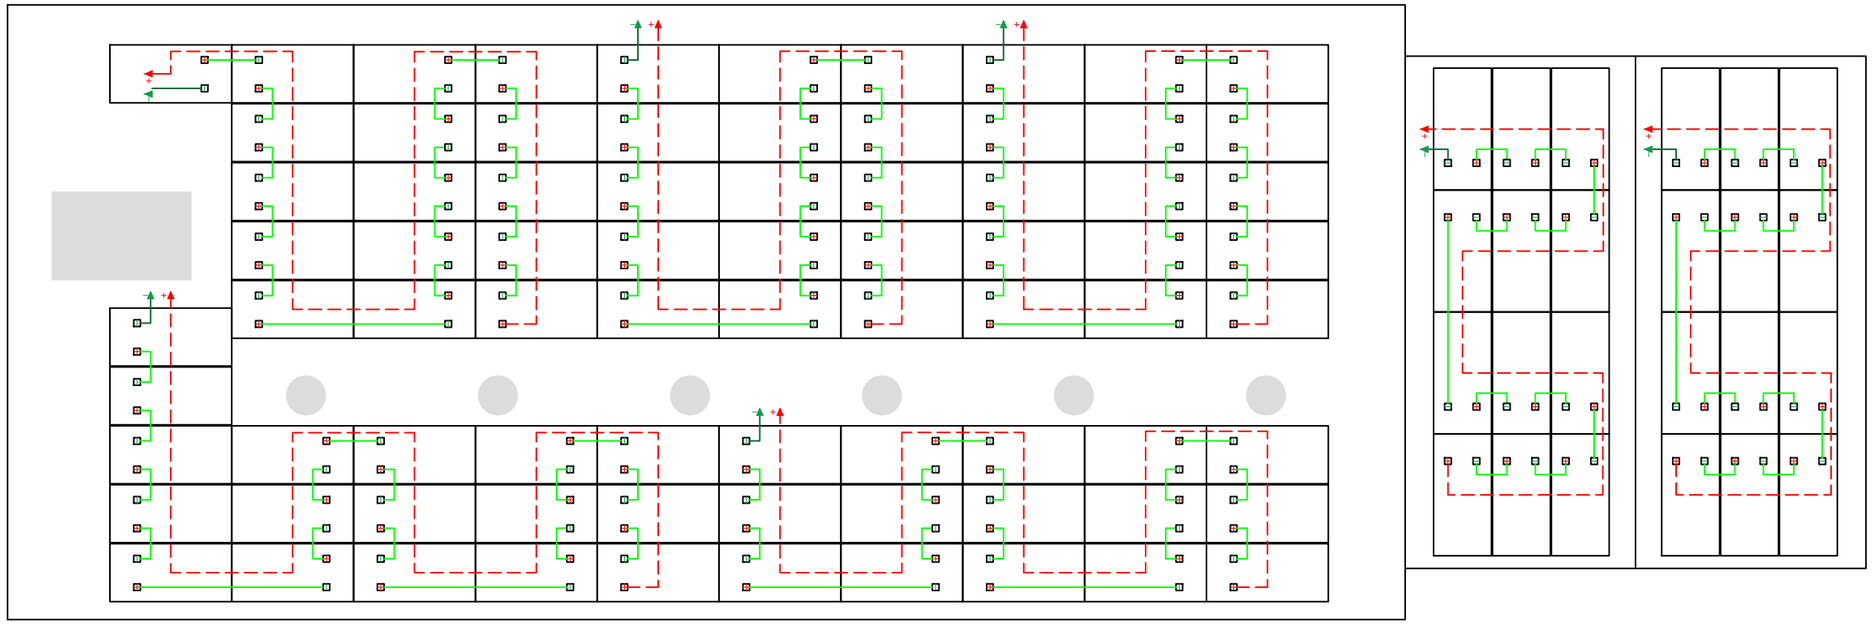



WIRING PV MODULE

SOLAR WING

บริษัท โซลาร์ วิง เอนเนอร์ยี จำกัด
555 หมู่ที่ 1 ต.นิคมสงเคราะห์
อ.เมืองอุดรธานี จ.อุดรธานี 41000

ARCHITECT	
CIVIL ENGINEER	
ศุภกันต์ นันทะเขต ภย. 100087	
ELECTRICAL ENGINEER	
ปาณสาน สินนอก ภฟก.71288	
วนิดา ถำวาปี ภฟก.70838	
SANUTARY ENGINEER	
PROJECT NO: SHOP DWG.	
PROJECT NAME: 65.79 kWp. SOLAR PV ROOFTOP	
PROJECT OWNER: น้ำดีมไอดอล	
DRAWN: ตะวัน ภฟก.72980	
CHECKED:	
APPROVED:	
SCALE:	1:120
DATE:	05/10/2026
DWG NO:	EE-04
SHEET NO:	

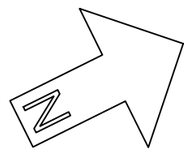

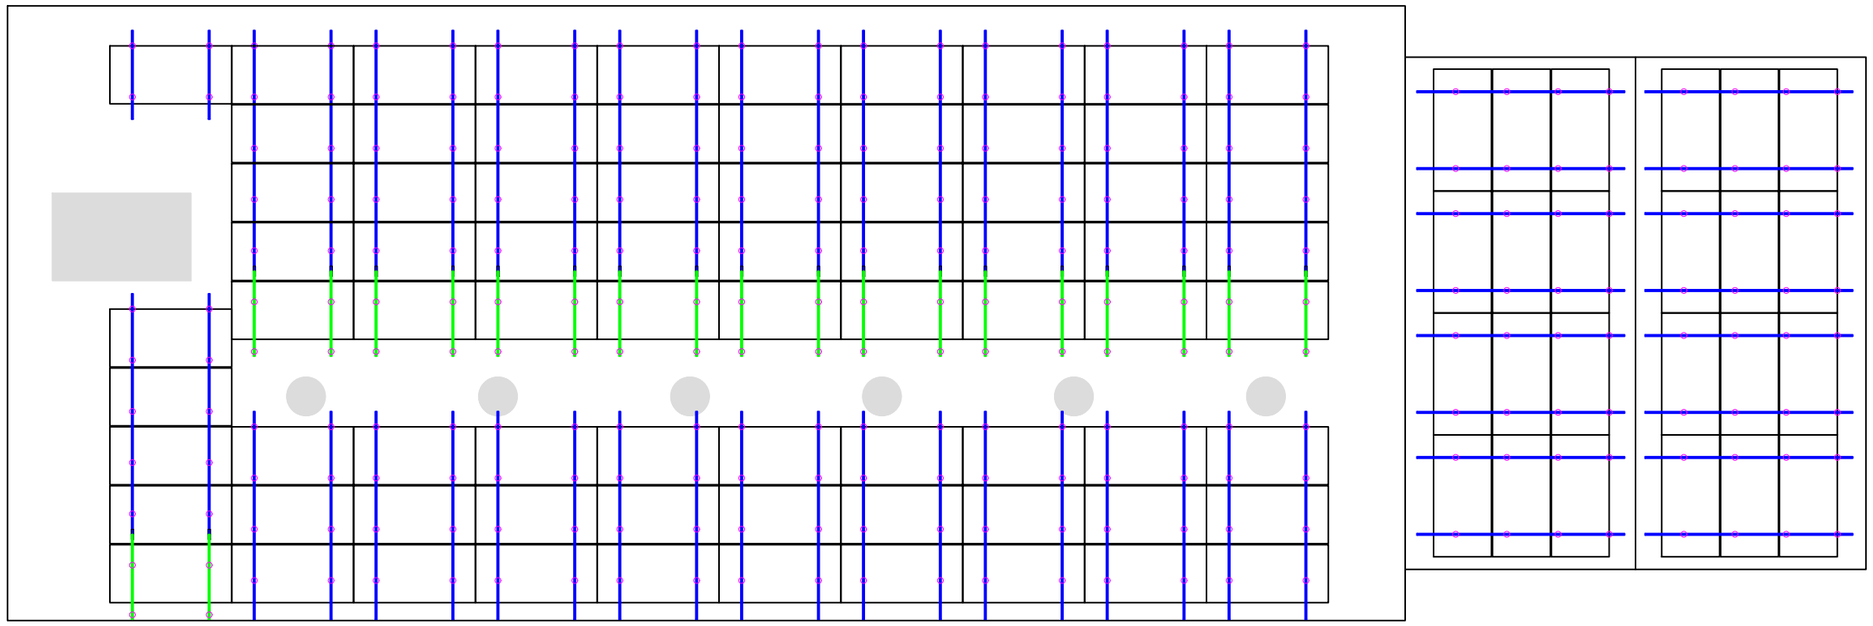

DETAIL MOUTHING STRUCTURE

SOLAR WING

บริษัท โซลาร์ วิง เอนเนอร์ยี จำกัด
555 หมู่ที่ 1 ต.นิคมสงเคราะห์
อ.เมืองอุดรธานี จ.อุดรธานี 41000

ARCHITECT

CIVIL ENGINEER


ELECTRICAL ENGINEER

ตะวัน กิตติอาสา ภฟก.72980


วนิดา ถ้ำวาปี ภฟก.70838

SANUTARY ENGINEER


PROJECT NO:	SHOP DWG.
PROJECT NAME:	65.79 kWp. SOLAR PV ROOFTOP
PROJECT OWNER:	น้ำตีมไอดอล
DRAWN:	ตะวัน ภฟก.72980
CHECKED:	
APPROVED:	
SCALE:	1:120
DATE:	05/10/2026
DWG NO:	EE-05
SHEET NO:	

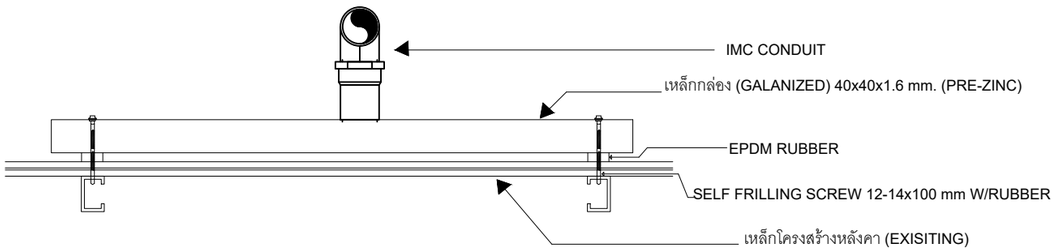


SECTION A

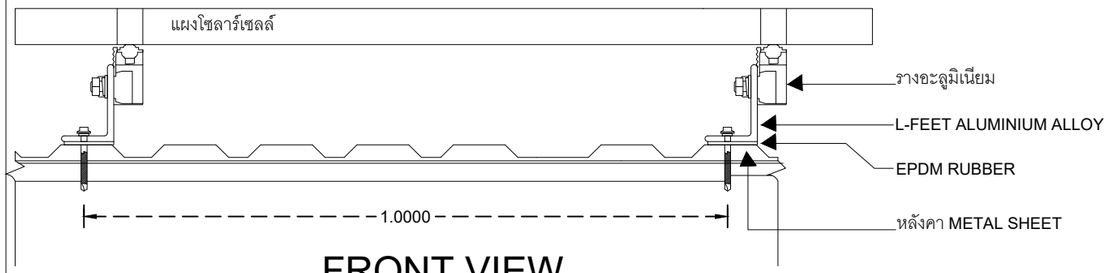

FRONT VIEW

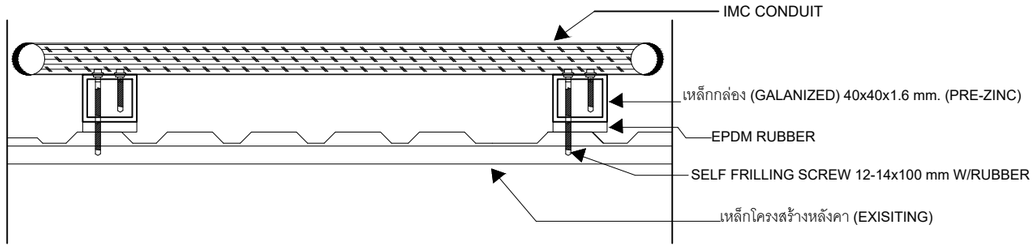

SECTION B

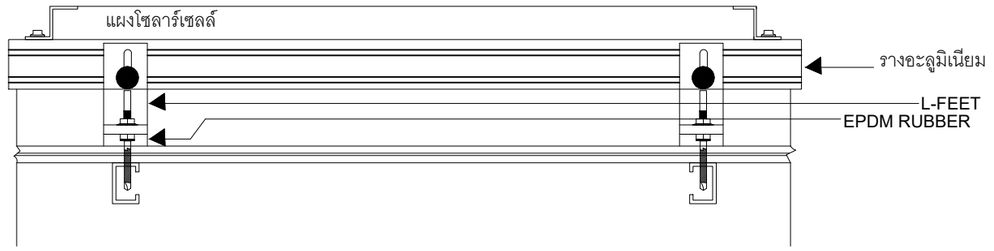

SLIDE VIEW

DETAIL SUPPORT IMC CONDUIT

แบบขยายการติดตั้ง แผงโซลาร์เซลล์

บริษัท โซลาร์ วิง เอนเนอร์ยี จำกัด
555 หมู่ที่ 1 ต.นิคมสงเคราะห์
อ.เมืองอุดรธานี จ.อุดรธานี 41000

ARCHITECT

CIVIL ENGINEER

ELECTRICAL ENGINEER

ตะวัน กิตติอาสา ภฟก.72980

วนิดา ถำวาปี ภฟก.70838

SANUTARY ENGINEER


PROJECT NO:
Drawing for Construction


PROJECT NAME:
65.79 kWp.
SOLAR PV ROOFTOP


PROJECT OWNER:
น้ำตีมไอดอล

DRAWN:
ตะวัน ภฟก.72980


CHECKED:	
APPROVED:	
SCALE:	NTS.
DATE:	05/10/2026
DWG NO:	EE-06
SHEET NO:	

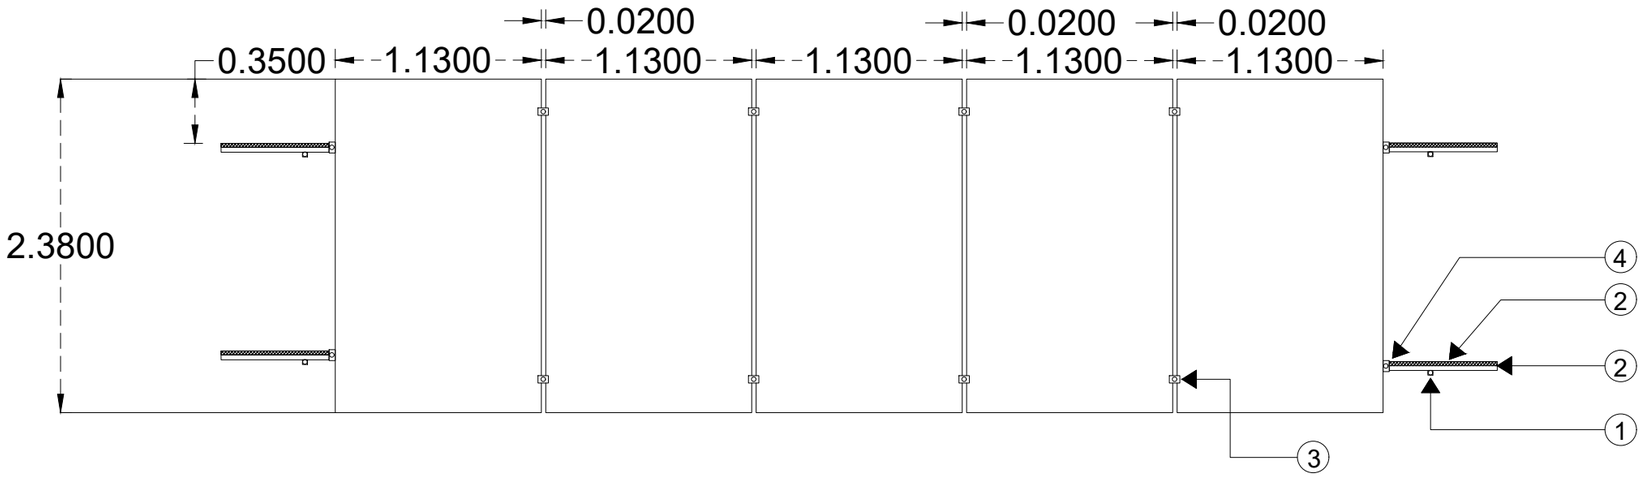

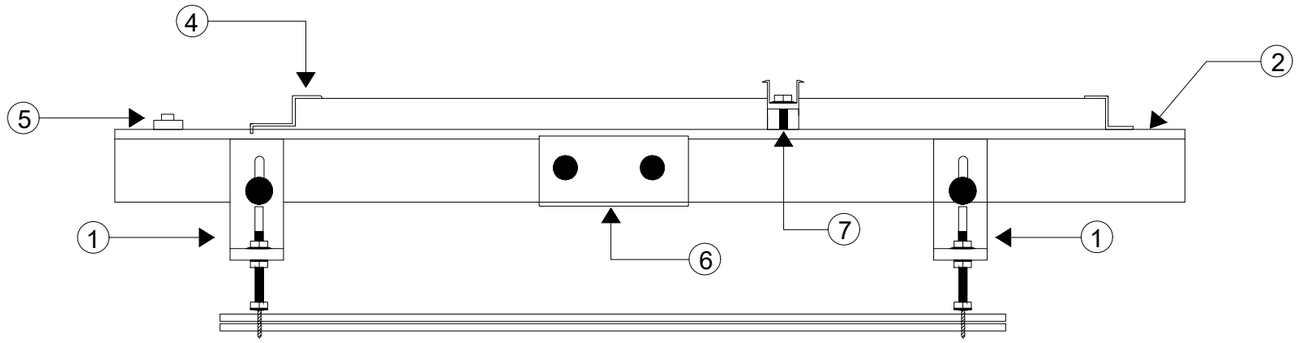

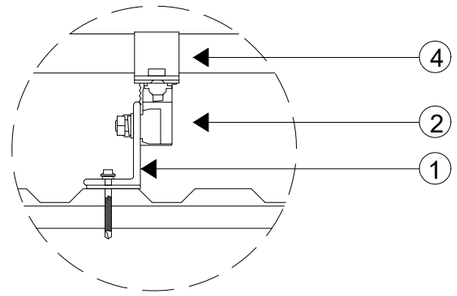


item	Model	Description	Meterial	Remark
1	GM-MRH-LDS-03	L-FEET	ALUMINIUM ALLOY	
2	GM-R02-LIGHT	RAIL	ANODIZED AL6005-T5	
3	GM-MC-30	MID CLAMP	ANODIZED AL6005-T5	
4	GM-EC-30	END CLAMP	ANODIZED AL6005-T5	
5	GM-EK	GROUND LUG	ANODIZED AL6005-T5/SUS 304	
6	GM-RS-01-L-150	RAIL JOINT PLATE	ALUMINIUM ALLOY&STAINLESS STEEL	
7	GM-E-EL-04	RAIL EARTHING CLIP	SUS 304	

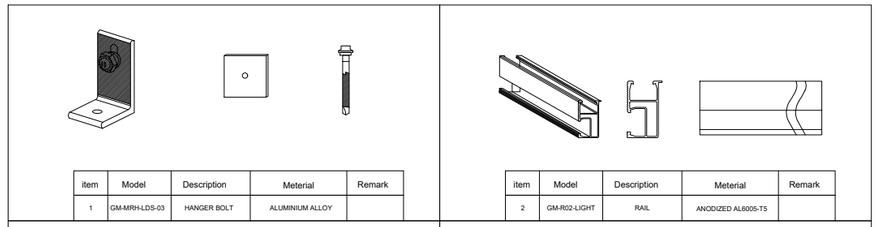


item	Model	Description	Meterial	Remark
1	GM-MRH-LDS-03	HANGER BOLT	ALUMINIUM ALLOY	

item	Model	Description	Meterial	Remark
2	GM-R02-LIGHT	RAIL	ANODIZED AL6005-T5	

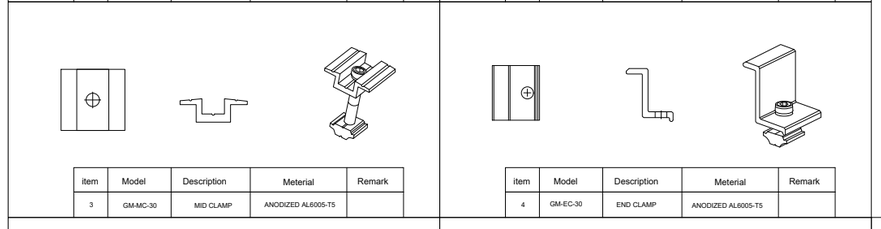


item	Model	Description	Meterial	Remark
3	GM-MC-30	MID CLAMP	ANODIZED AL6005-T5	

item	Model	Description	Meterial	Remark
4	GM-EC-30	END CLAMP	ANODIZED AL6005-T5	

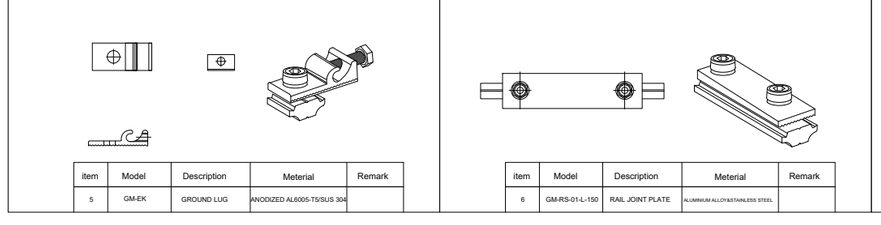

item	Model	Description	Meterial	Remark
5	GM-EK	GROUND LUG	ANODIZED AL6005-T5/SUS 304	

item	Model	Description	Meterial	Remark
6	GM-RS-01-L-150	RAIL JOINT PLATE	ALUMINIUM ALLOY&STAINLESS STEEL	

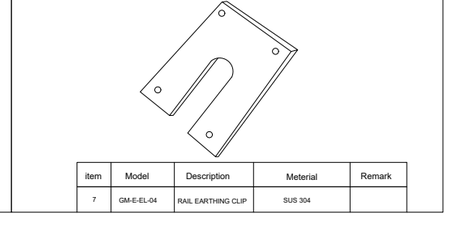

item	Model	Description	Meterial	Remark
7	GM-E-EL-04	RAIL EARTHING CLIP	SUS 304	

SOLAR WING

บริษัท โซลาร์ วิง เอนเนอร์ยี จำกัด
555 หมู่ที่ 1 ต.นิคมสงเคราะห์
อ.เมืองอุดรธานี จ.อุดรธานี 41000

ARCHITECT

CIVIL ENGINEER

ELECTRICAL ENGINEER

ตะวัน กิตติอาสา ภฟก.72980

วนิดา ถำวาปี ภฟก.70838

SANUTARY ENGINEER

PROJECT NO:

Drawing for Construction

PROJECT NAME:

65.79 kWp.
SOLAR PV ROOFTOP

PROJECT OWNER:

น้ำตีมไอดอล

DRAWN:

ตะวัน ภฟก.72980

CHECKED:	
APPROVED:	
SCALE:	NTS.
DATE:	05/10/2026
DWG NO:	EE-07
SHEET NO:	