แบบติดตั้งระบบผลิตไฟฟ้าด้วยเซลล์แสงอาทิตย์บนหลังคาขนาด 10.32 kWp.


ดีเอมซี คลินิกเวชกรรม - หมอบอส


PV-SOLAR ROOFTOP

SHOP DWG.

Date: 15 October 2026

SOLAR WING ENERGY CO.,LTD
555 Nikhom Song Khor,Mueang Udon Thani District,
Udon Thani 41000
Tel.080-329-9777

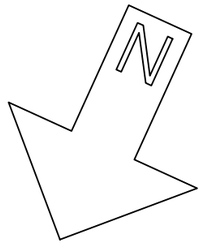

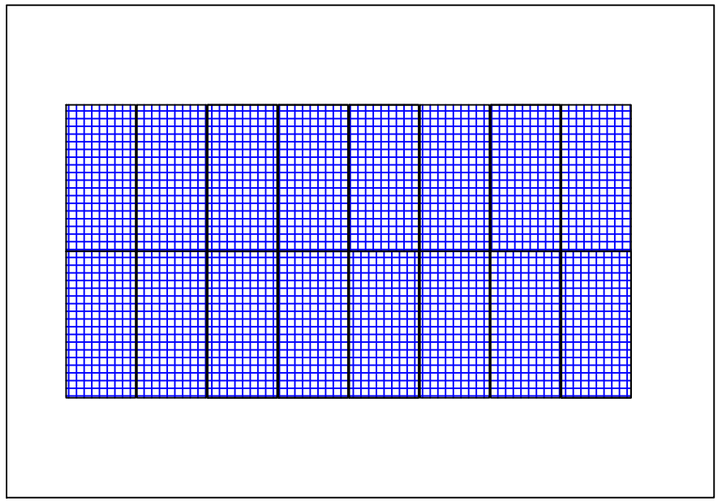

NOTE:

PV MODULE

INVERTER 10 kW | PV-MDB | LC (EXISITING)

PV MODULE AND STRING INVERTER DESCRIPTION

	NAME : PV Module Type : Mono Halfcell-cut 645 Wp Brand : LONGI
	NAME : String Inverter Brand : Huawei Model : SUN2000-10K-MAP0 System Voltage : 380/400 V Frequency : 50Hz Protection : DC Disconnecting Switch AC Overcurrent, Anti-Islanding, DC Revers polarity ,DC and AC Surge arrester Residual Current monitoring

SUMMARY FOR INVERTER	
MODULE TYPE	645 Wp
PV MODULE	16 MODULE
NUMBER OF MODULE/STRING	16 MODULE
TOTAL OF STRING	1 STRING
INSTALL CAPACITY	10.32 kWp
INVERTER RATED	10 kW
NUMBER OF INVERTER	1 UNIT



แผนที่โดยสังเขป : 17.426668840028448, 102.77684397146686

SOLAR WING

บริษัท โซลาร์ วิง เอนเนอร์ยี จำกัด
555 หมู่ที่ 1 ต.นิคมสงเคราะห์
อ.เมืองอุดรธานี จ.อุดรธานี 41000

ARCHITECT

CIVIL ENGINEER


ELECTRICAL ENGINEER


ตะวัน กิตติอาสา ภฟก.72980

วนิดา ถำวาปี ภฟก.70838

SANUTARY ENGINEER

PROJECT NO:	SHOP DWG.
PROJECT NAME:	10.32 kWp. SOLAR PV ROOFTOP
PROJECT OWNER:	ดีเอมซี คลินิกเวชกรรม
DRAWN:	ตะวัน ภฟก.72980
CHECKED:	
APPROVED:	
SCALE:	1:150
DATE:	15/10/2026
DWG NO:	EE-01
SHEET NO:	

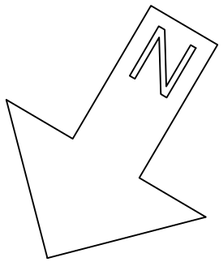

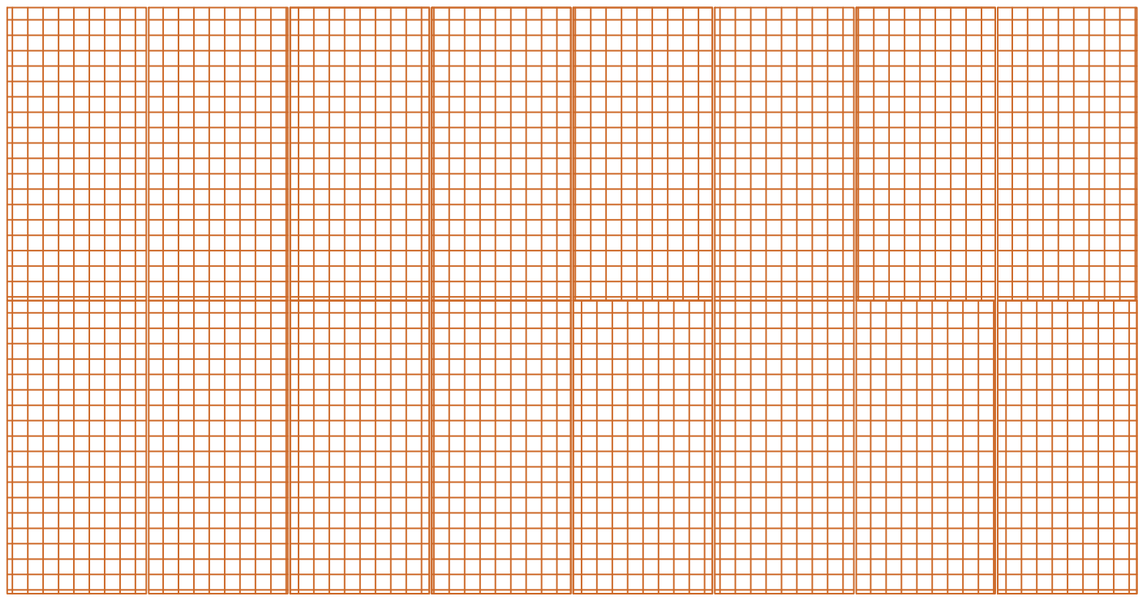


DESIGN PV MODULE

SOLAR WING

บริษัท โซลาร์ วิง เอนเนอร์ยี จำกัด
555 หมู่ที่ 1 ต.นิคมสงเคราะห์
อ.เมืองอุดรธานี จ.อุดรธานี 41000

ARCHITECT	
CIVIL ENGINEER	
ELECTRICAL ENGINEER	ตะวัน กิตติอาสา ภฟก.72980
	วนิดา ถำวาปี ภฟก.70838
SANUTARY ENGINEER	
PROJECT NO:	SHOP DWG.
PROJECT NAME:	10.32 kWp. SOLAR PV ROOFTOP
PROJECT OWNER:	ดีเอมซี คลินิกเวชกรรม
DRAWN:	ตะวัน ภฟก.72980
CHECKED:	
APPROVED:	
SCALE:	1:75
DATE:	15/10/2026
DWG NO:	EE-02
SHEET NO:	

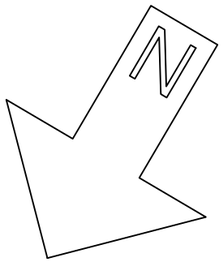

INV - 10KTL STR1 PV 8	INV - 10KTL STR1 PV 7	INV - 10KTL STR1 PV 6	INV - 10KTL STR1 PV 5	INV - 10KTL STR1 PV 4	INV - 10KTL STR1 PV 3	INV - 10KTL STR1 PV 2	INV - 10KTL STR1 PV 1
INV - 10KTL STR1 PV 9	INV - 10KTL STR1 PV 10	INV - 10KTL STR1 PV 11	INV - 10KTL STR1 PV 12	INV - 10KTL STR1 PV 13	INV - 10KTL STR1 PV 14	INV - 10KTL STR1 PV 15	INV - 10KTL STR1 PV 16

NUMBER OF MODULE/STRING

SOLAR WING

บริษัท โซลาร์ วิง เอนเนอร์ยี จำกัด
555 หมู่ที่ 1 ต.นิคมสงเคราะห์
อ.เมืองอุดรธานี จ.อุดรธานี 41000

ARCHITECT

CIVIL ENGINEER

ELECTRICAL ENGINEER

ตะวัน กิตติอาสา ภฟก.72980

วนิดา ถำวาปี ภฟก.70838

SANUTARY ENGINEER


PROJECT NO:
SHOP DWG.


PROJECT NAME:
10.32 kWp.
SOLAR PV ROOFTOP

PROJECT OWNER:
ดีเอมซี คลินิกเวชกรรม

DRAWN:
ตะวัน ภฟก.72980

CHECKED:	
APPROVED:	
SCALE:	1:75
DATE:	15/10/2026
DWG NO:	EE-03
SHEET NO:	

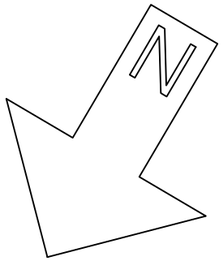

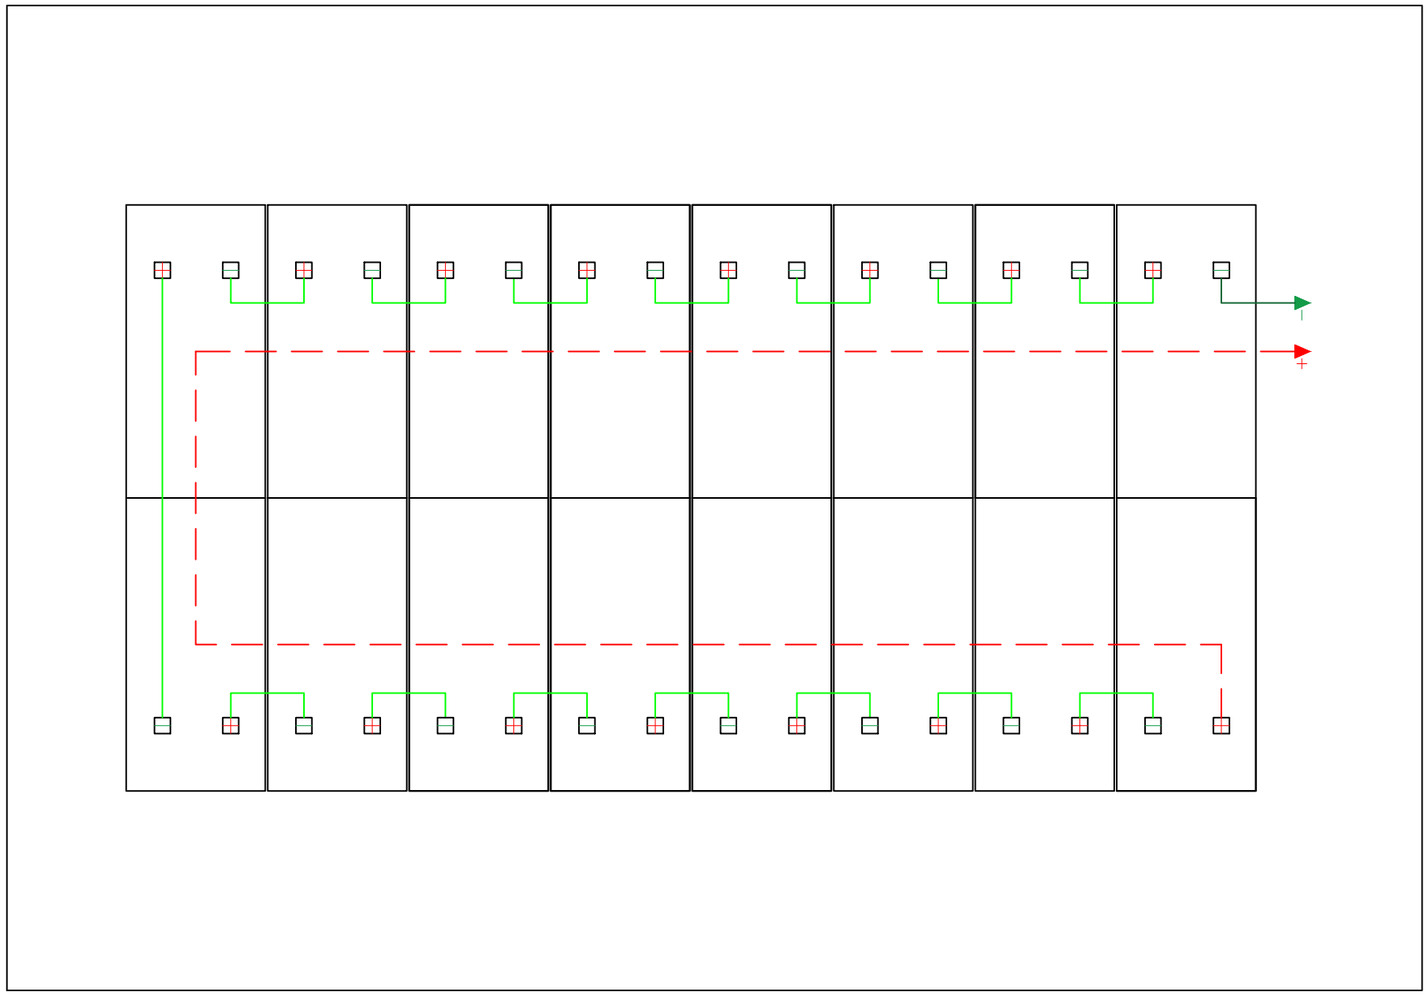



WIRING PV MODULE

SOLAR WING

บริษัท โซลาร์ วิง เอนเนอร์ยี จำกัด
555 หมู่ที่ 1 ต.นิคมสงเคราะห์
อ.เมืองอุดรธานี จ.อุดรธานี 41000

ARCHITECT	
CIVIL ENGINEER	
ELECTRICAL ENGINEER	ตะวัน กิตติอาสา ภฟก.72980
	วนิดา ถำวาปี ภฟก.70838
SANUTARY ENGINEER	
PROJECT NO:	SHOP DWG.
PROJECT NAME:	10.32 kWp. SOLAR PV ROOFTOP
PROJECT OWNER:	ดีเอมซี คลินิกเวชกรรม
DRAWN:	ตะวัน ภฟก.72980
CHECKED:	
APPROVED:	
SCALE:	1:75
DATE:	15/10/2026
DWG NO:	EE-04
SHEET NO:	

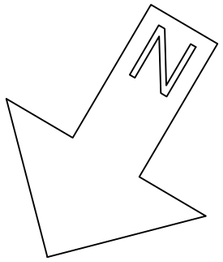

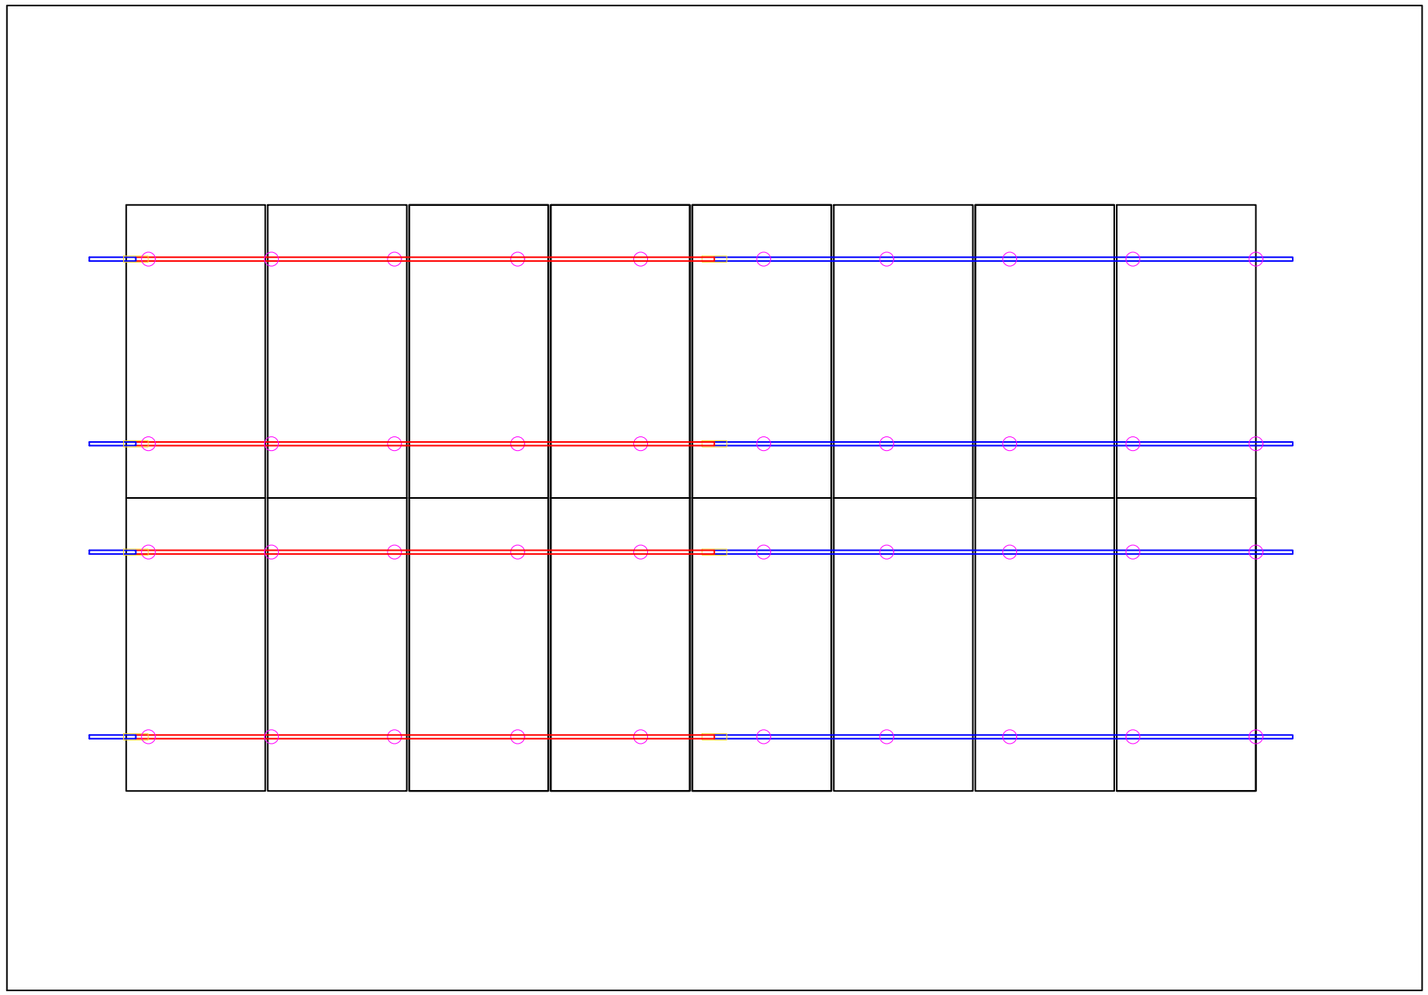


DETAIL MOUTHING STRUCTURE


SOLAR WING

บริษัท โซลาร์ วิง เอนเนอร์ยี จำกัด
555 หมู่ที่ 1 ต.นิคมสงเคราะห์
อ.เมืองอุดรธานี จ.อุดรธานี 41000


ARCHITECT	
CIVIL ENGINEER	
ELECTRICAL ENGINEER	ตะวัน กิตติอาสา ภฟก.72980
	วนิดา ถำวาปี ภฟก.70838
SANUTARY ENGINEER	
PROJECT NO:	SHOP DWG.
PROJECT NAME:	10.32 kWp. SOLAR PV ROOFTOP
PROJECT OWNER:	ดีเอมซี คลินิกเวชกรรม
DRAWN:	ตะวัน ภฟก.72980
CHECKED:	
APPROVED:	
SCALE:	1:75
DATE:	15/10/2026
DWG NO:	EE-05
SHEET NO:	

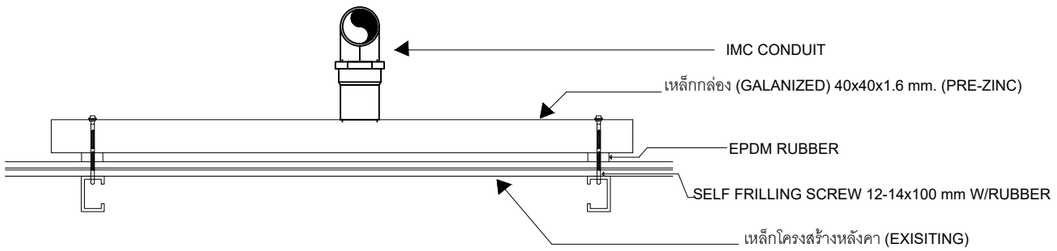


SECTION A

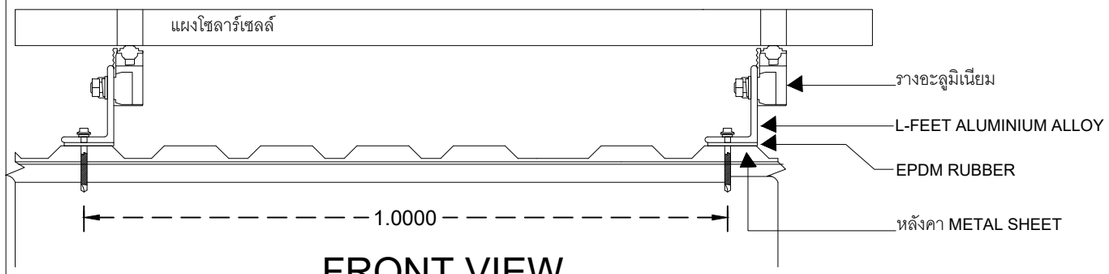

FRONT VIEW

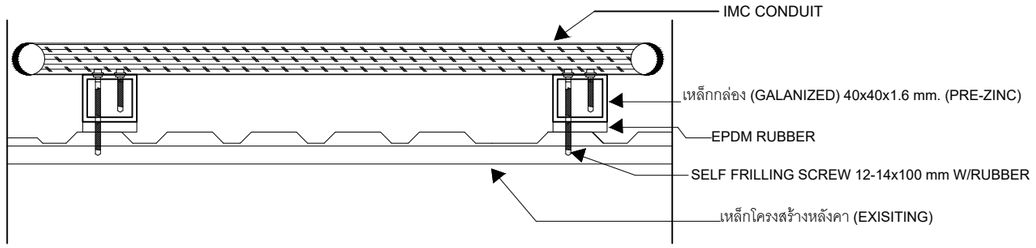

SECTION B

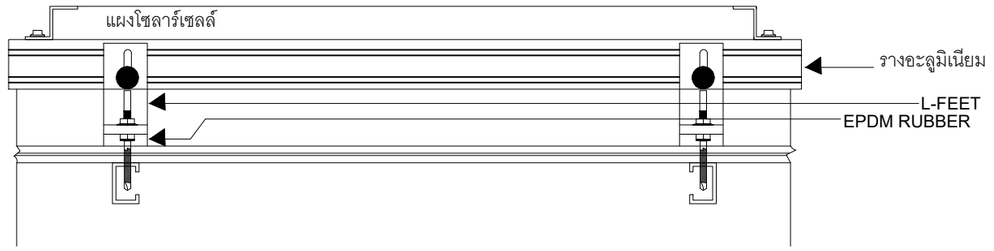

SLIDE VIEW

DETAIL SUPPORT IMC CONDUIT

แบบขยายการติดตั้ง แผงโซลาร์เซลล์

บริษัท โซลาร์ วิง เอนเนอร์ยี จำกัด
555 หมู่ที่ 1 ต.นิคมสงเคราะห์
อ.เมืองอุดรธานี จ.อุดรธานี 41000

ARCHITECT

CIVIL ENGINEER

ELECTRICAL ENGINEER

ตะวัน กิตติอาสา ภฟก.72980

วนิดา ถำวาปี ภฟก.70838

SANUTARY ENGINEER


PROJECT NO:
SHOP DWG.


PROJECT NAME:
10.32 kWp.
SOLAR PV ROOFTOP


PROJECT OWNER:
ดีเอมซี คลินิกเวชกรรม

DRAWN:
ตะวัน ภฟก.72980


CHECKED:	
APPROVED:	
SCALE:	NTS.
DATE:	15/10/2026
DWG NO:	EE-06
SHEET NO:	

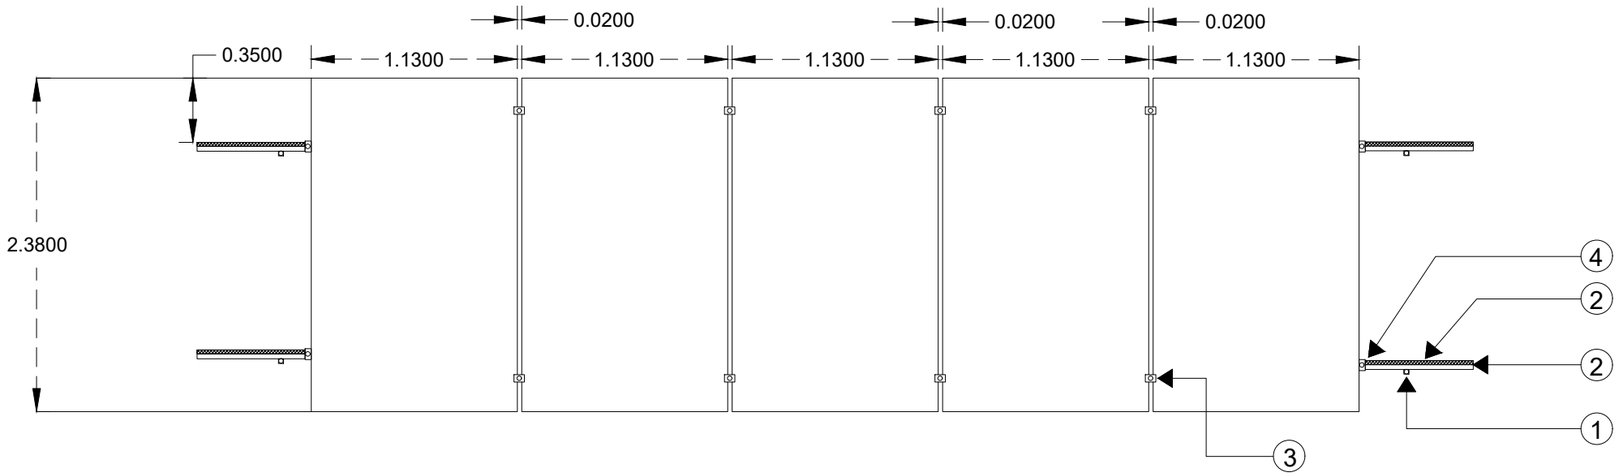

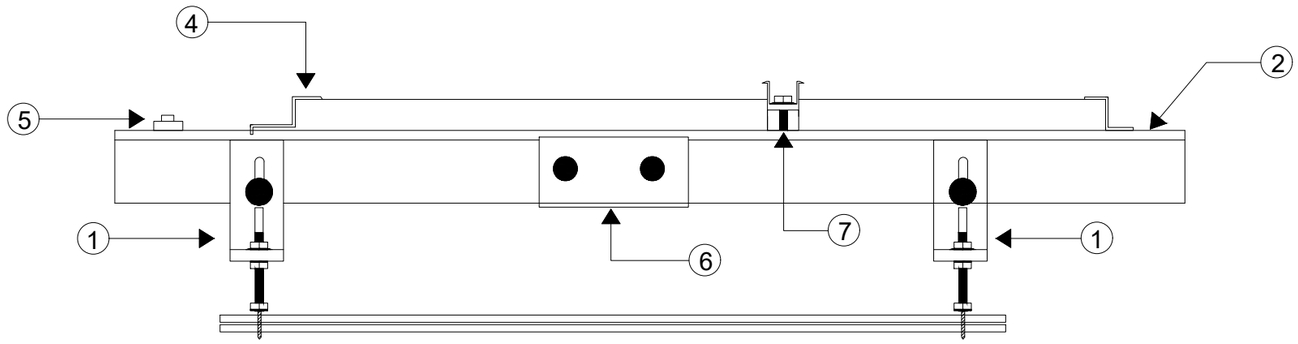

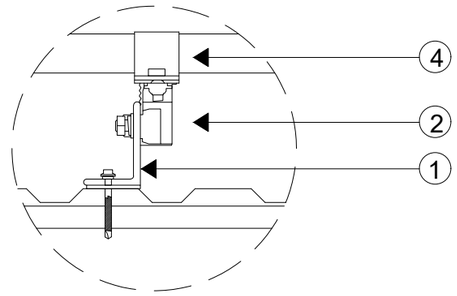


item	Model	Description	Meterial	Remark
1	GM-MRH-LDS-03	L-FEET	ALUMINIUM ALLOY	
2	GM-R02-LIGHT	RAIL	ANODIZED AL6005-T5	
3	GM-MC-30	MID CLAMP	ANODIZED AL6005-T5	
4	GM-EC-30	END CLAMP	ANODIZED AL6005-T5	
5	GM-EK	GROUND LUG	ANODIZED AL6005-T5/SUS 304	
6	GM-RS-01-L-150	RAIL JOINT PLATE	ALUMINIUM ALLOY&STAINLESS STEEL	
7	GM-E-EL-04	RAIL EARTHING CLIP	SUS 304	

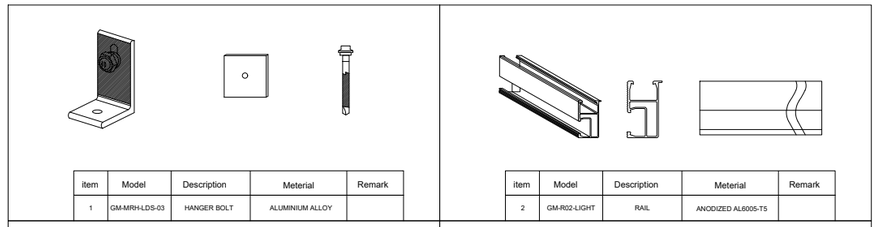


item	Model	Description	Meterial	Remark
1	GM-MRH-LDS-03	HANGER BOLT	ALUMINIUM ALLOY	

item	Model	Description	Meterial	Remark
2	GM-R02-LIGHT	RAIL	ANODIZED AL6005-T5	

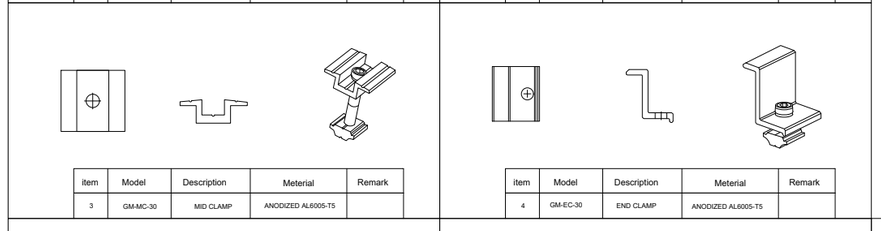


item	Model	Description	Meterial	Remark
3	GM-MC-30	MID CLAMP	ANODIZED AL6005-T5	

item	Model	Description	Meterial	Remark
4	GM-EC-30	END CLAMP	ANODIZED AL6005-T5	

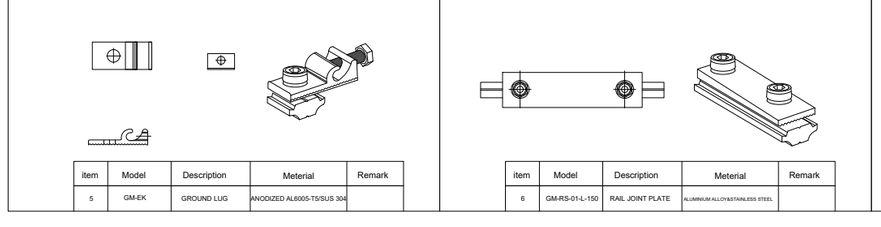

item	Model	Description	Meterial	Remark
5	GM-EK	GROUND LUG	ANODIZED AL6005-T5/SUS 304	

item	Model	Description	Meterial	Remark
6	GM-RS-01-L-150	RAIL JOINT PLATE	ALUMINIUM ALLOY&STAINLESS STEEL	

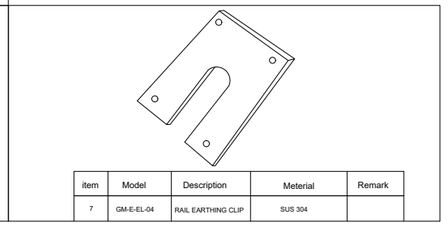

item	Model	Description	Meterial	Remark
7	GM-E-EL-04	RAIL EARTHING CLIP	SUS 304	

บริษัท โซลาร์ วิง เอนเนอร์ยี จำกัด
555 หมู่ที่ 1 ต.นิคมสงเคราะห์
อ.เมืองอุดรธานี จ.อุดรธานี 41000

ARCHITECT

CIVIL ENGINEER

ELECTRICAL ENGINEER

ตะวัน กิตติอาสา ภฟก.72980

วนิดา ถำวาปี ภฟก.70838

SANUTARY ENGINEER

PROJECT NO:

SHOP DWG.

PROJECT NAME:

10.32 kWp.
SOLAR PV ROOFTOP

PROJECT OWNER:

ดีเอมซี คลินิกเวชกรรม

DRAWN:

ตะวัน ภฟก.72980

CHECKED:	
APPROVED:	
SCALE:	NTS.
DATE:	15/10/2026
DWG NO:	EE-07
SHEET NO:	